


 FANSHAWE	Prepared By: Facilities Management & Community Safety 1001 Fanshawe College Boulevard, London, ON, Canada N5Y 5R6	Title: D Building Second Floor 1001 Fanshawe College Blvd.	
		Issue Date: SEPT. 2019	Verified Date: SEPT. 2019
		Scale: NTS	

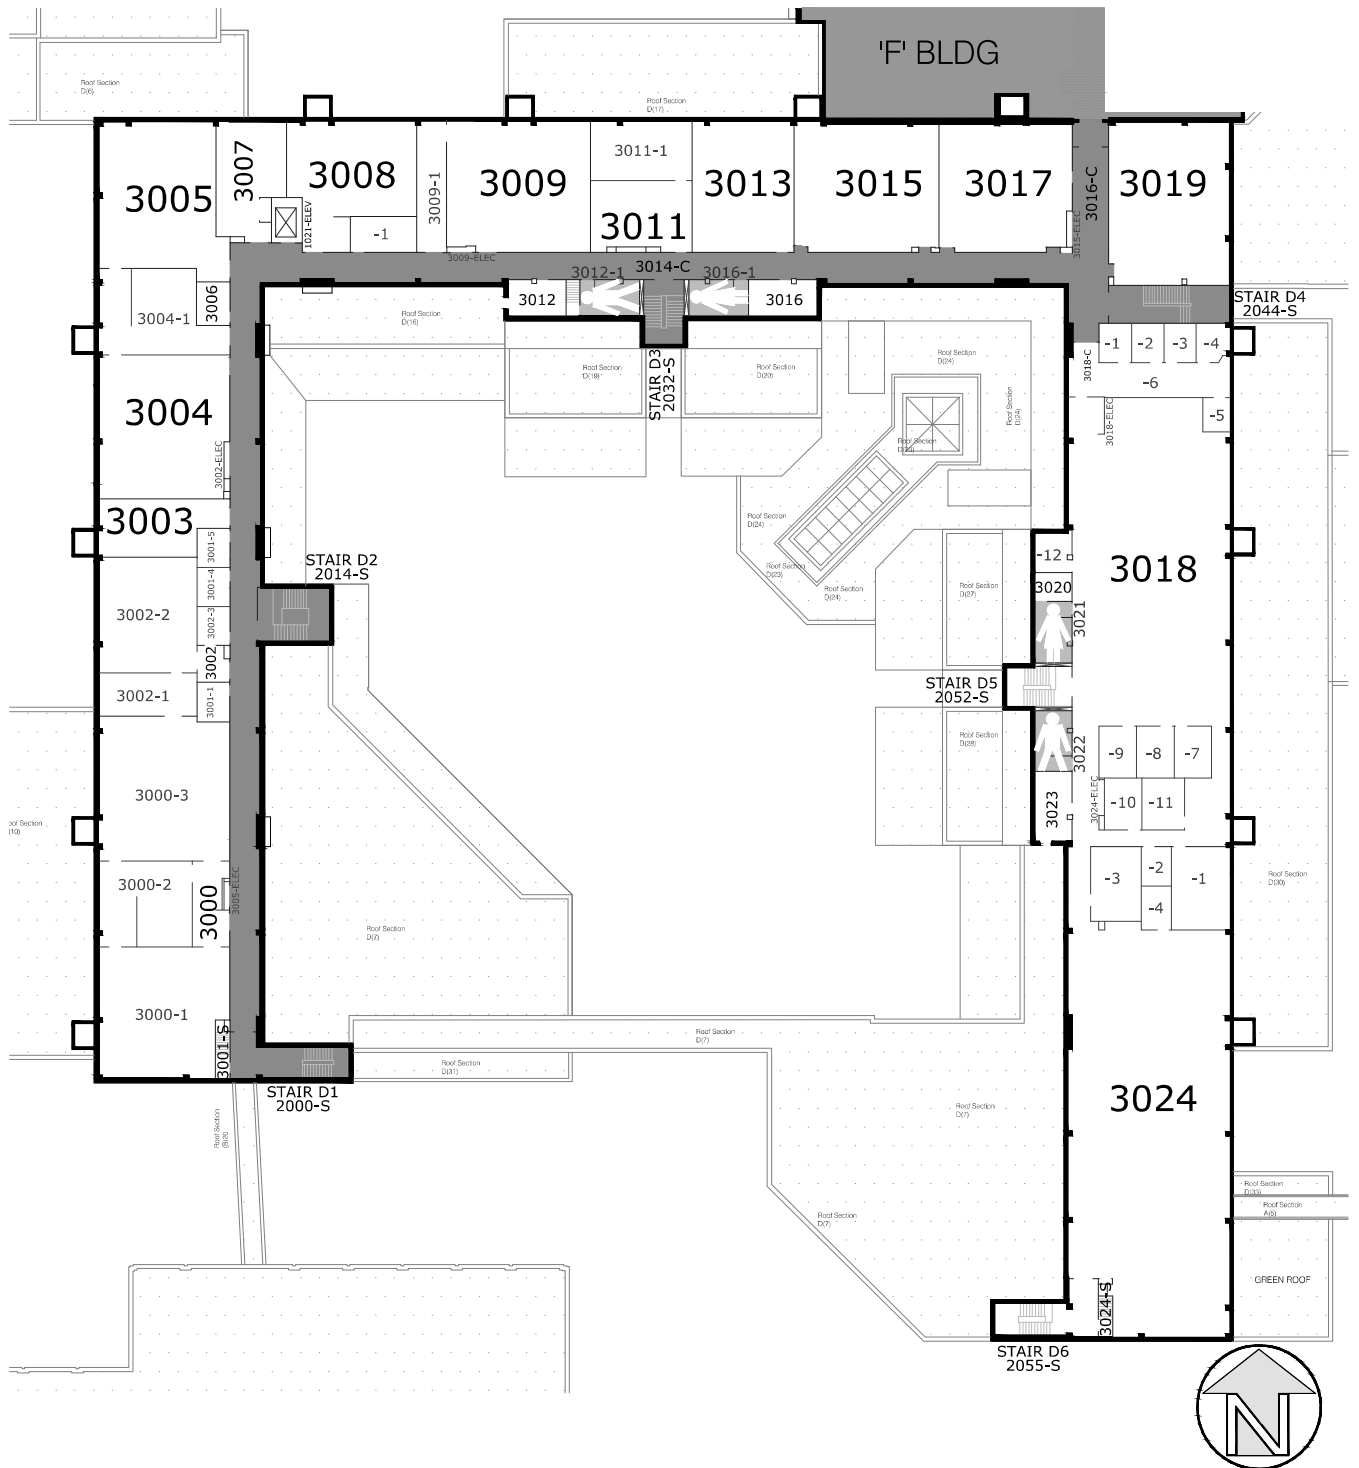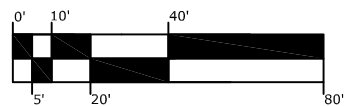

Prepared By:
Facilities Management &
Community Safety
1001 Fanshawe College Boulevard,
London, ON, Canada N5Y 5R6

Title: D Building Third Floor
1001 Fanshawe College Blvd.
Issue Date: NOV 2023 **Verified Date:** NOV 2023
Scale: NTS

D3

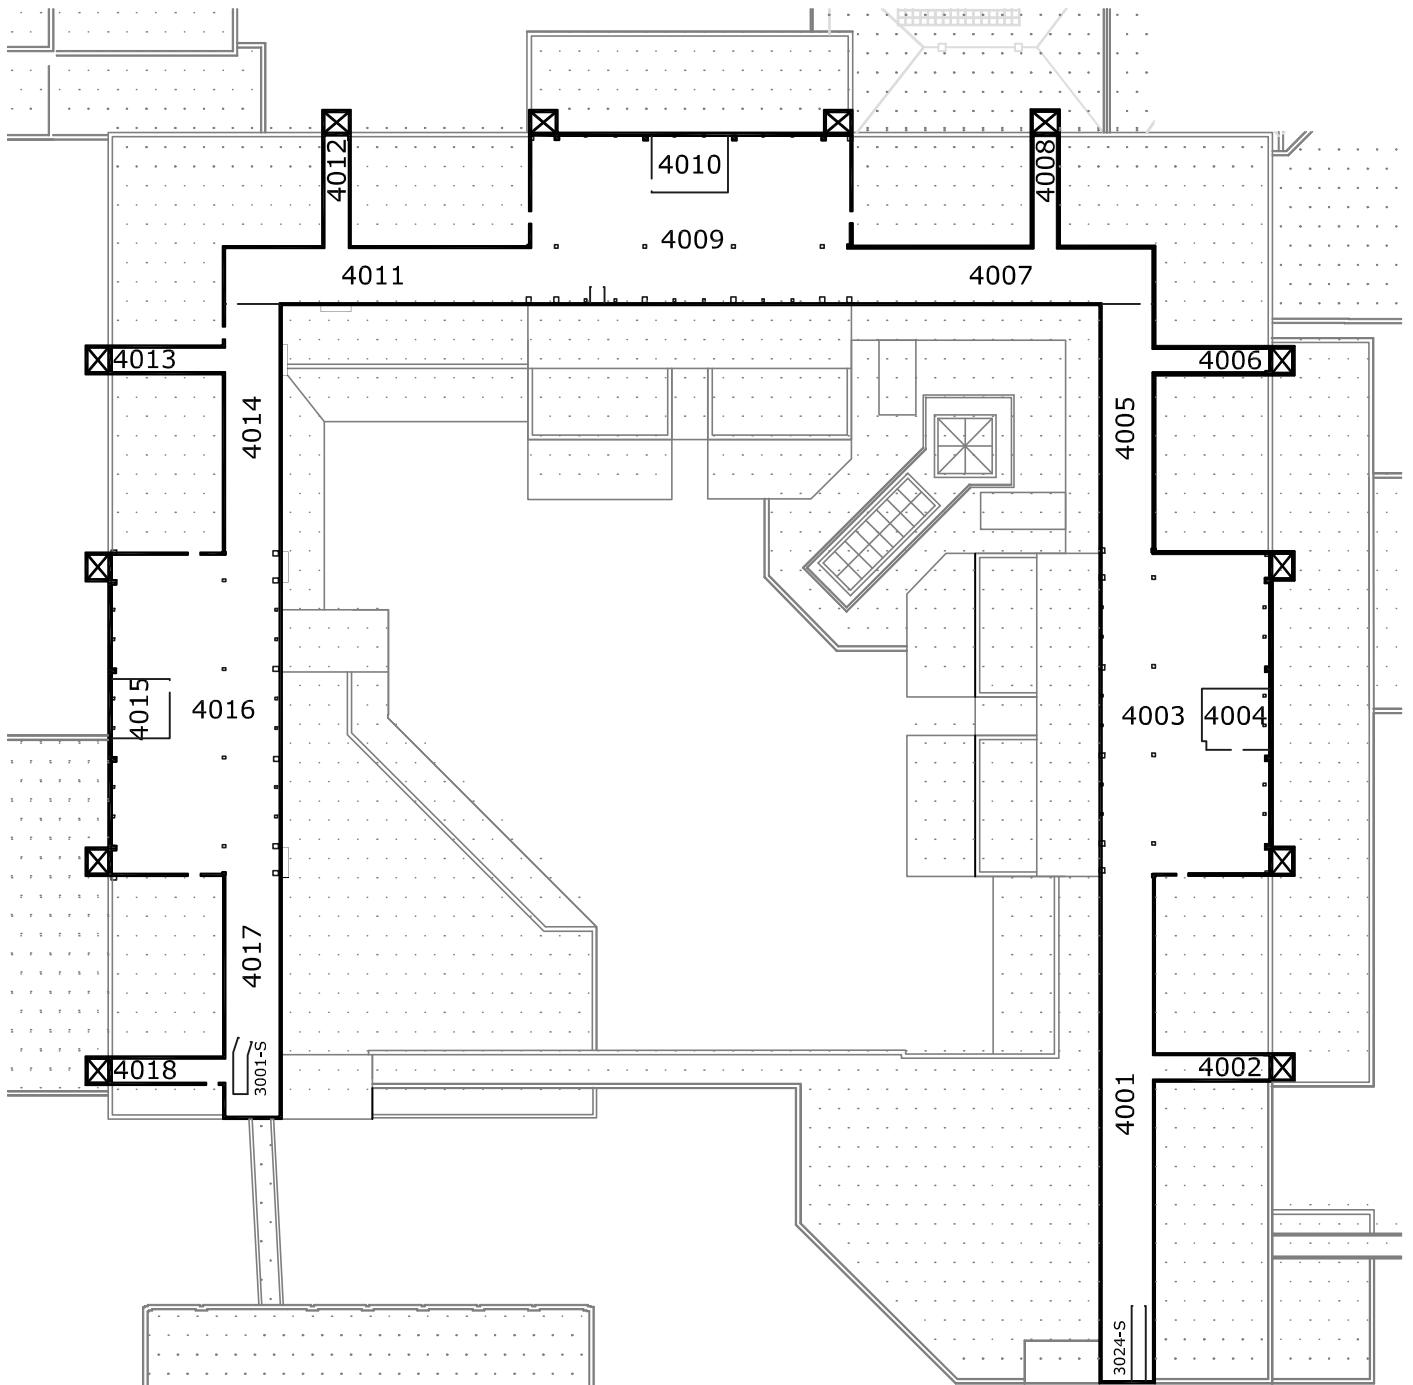

Prepared By:

**Facilities Management &
Community Safety**

1001 Fanshawe College Boulevard,
London, ON, Canada N5Y 5R6

Title: D Building Fourth Floor Penthouse
1001 Fanshawe College Blvd.

Issue Date: DEC 2015

Verified Date: SEPT 2018

Scale: NTS

D4